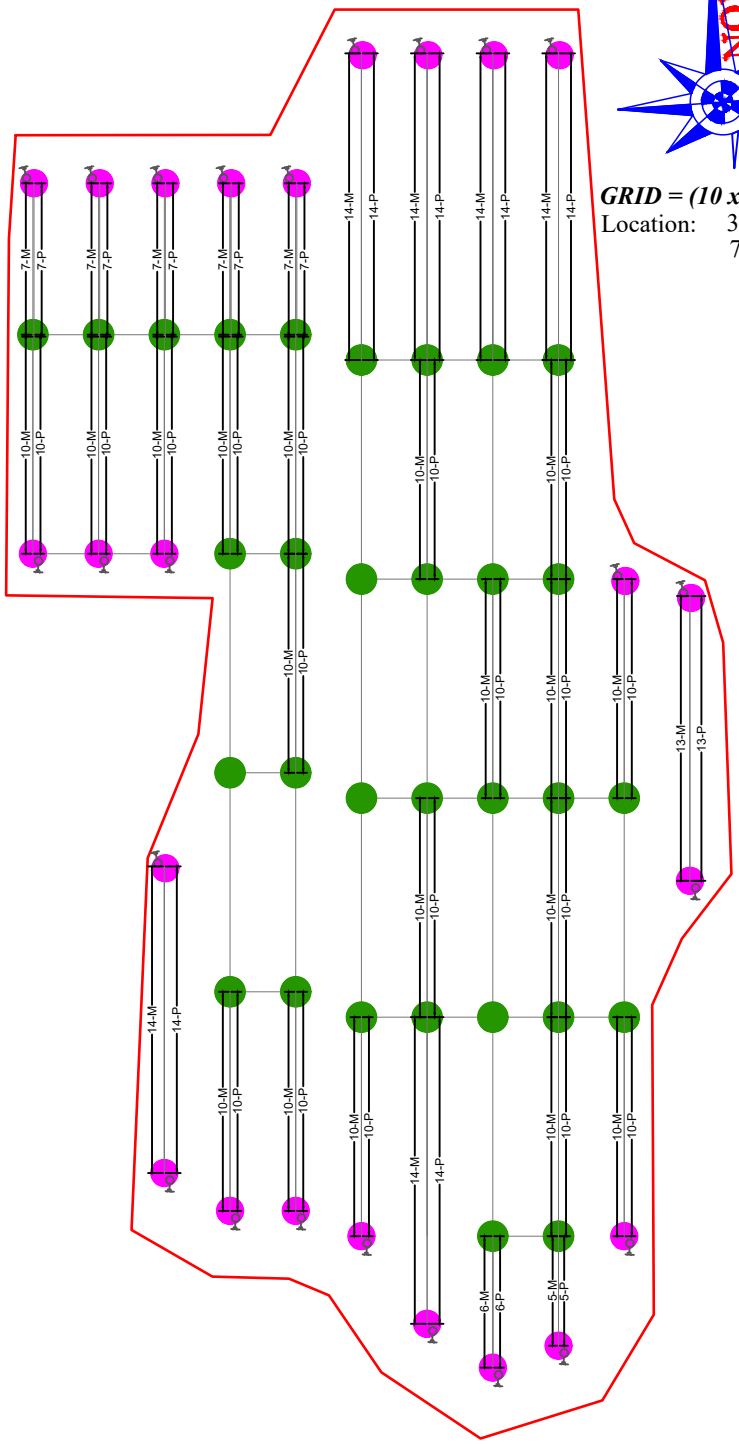

NORTH

GRID = (10 x 3) M

Location: 33.738978
74.964532
OR
SHAH
Enclave

EXTRA: 11 Anchors & 13 Poles

HEAD POSTS		24	No.s
INTERMEDIATE POSTS		0	No.s
ANCHORS		31	No.s
WATER SOURCE		24	No.s
GAPS		01	No.s
NO OF PLANTS		43	No.s
FRUITING WIRE		433	No.s
WIRE ROPE 8MM		1780	Mtrs
CLAMPS		120	MTRS
LOCKING CLAMP		24	No.s
GRIPPLE LOCKS		96	No.s
POST HOOKS		48	No.s
LATERAL PIPE		124	No.s
DRIPPERS (2/PLANT)		490	Mtrs
		866	No.s

GROWER's NAME : Syed Sinan Shah
ADDRESS : Reban Shopian
TOTAL AREA : 2 Kanals 12 MARLA
COVERED : 2 Kanals 12 MARLA
CONTACT No : 9797746344

M	Meter
P	Plant

GROWERS ID :
A-N 24-25-377

ISSUED FOR

DRAWN BY	DATE
Er. ASLAM JAMAL	12-10-2024

ABRAQ NURSERIES LLP
WAZBAGH HYDERPORA; SRINAGAR, J&K-190014
PHONE:-+91-9596961010 E-MAIL- nurseries@abraq.in

PX10